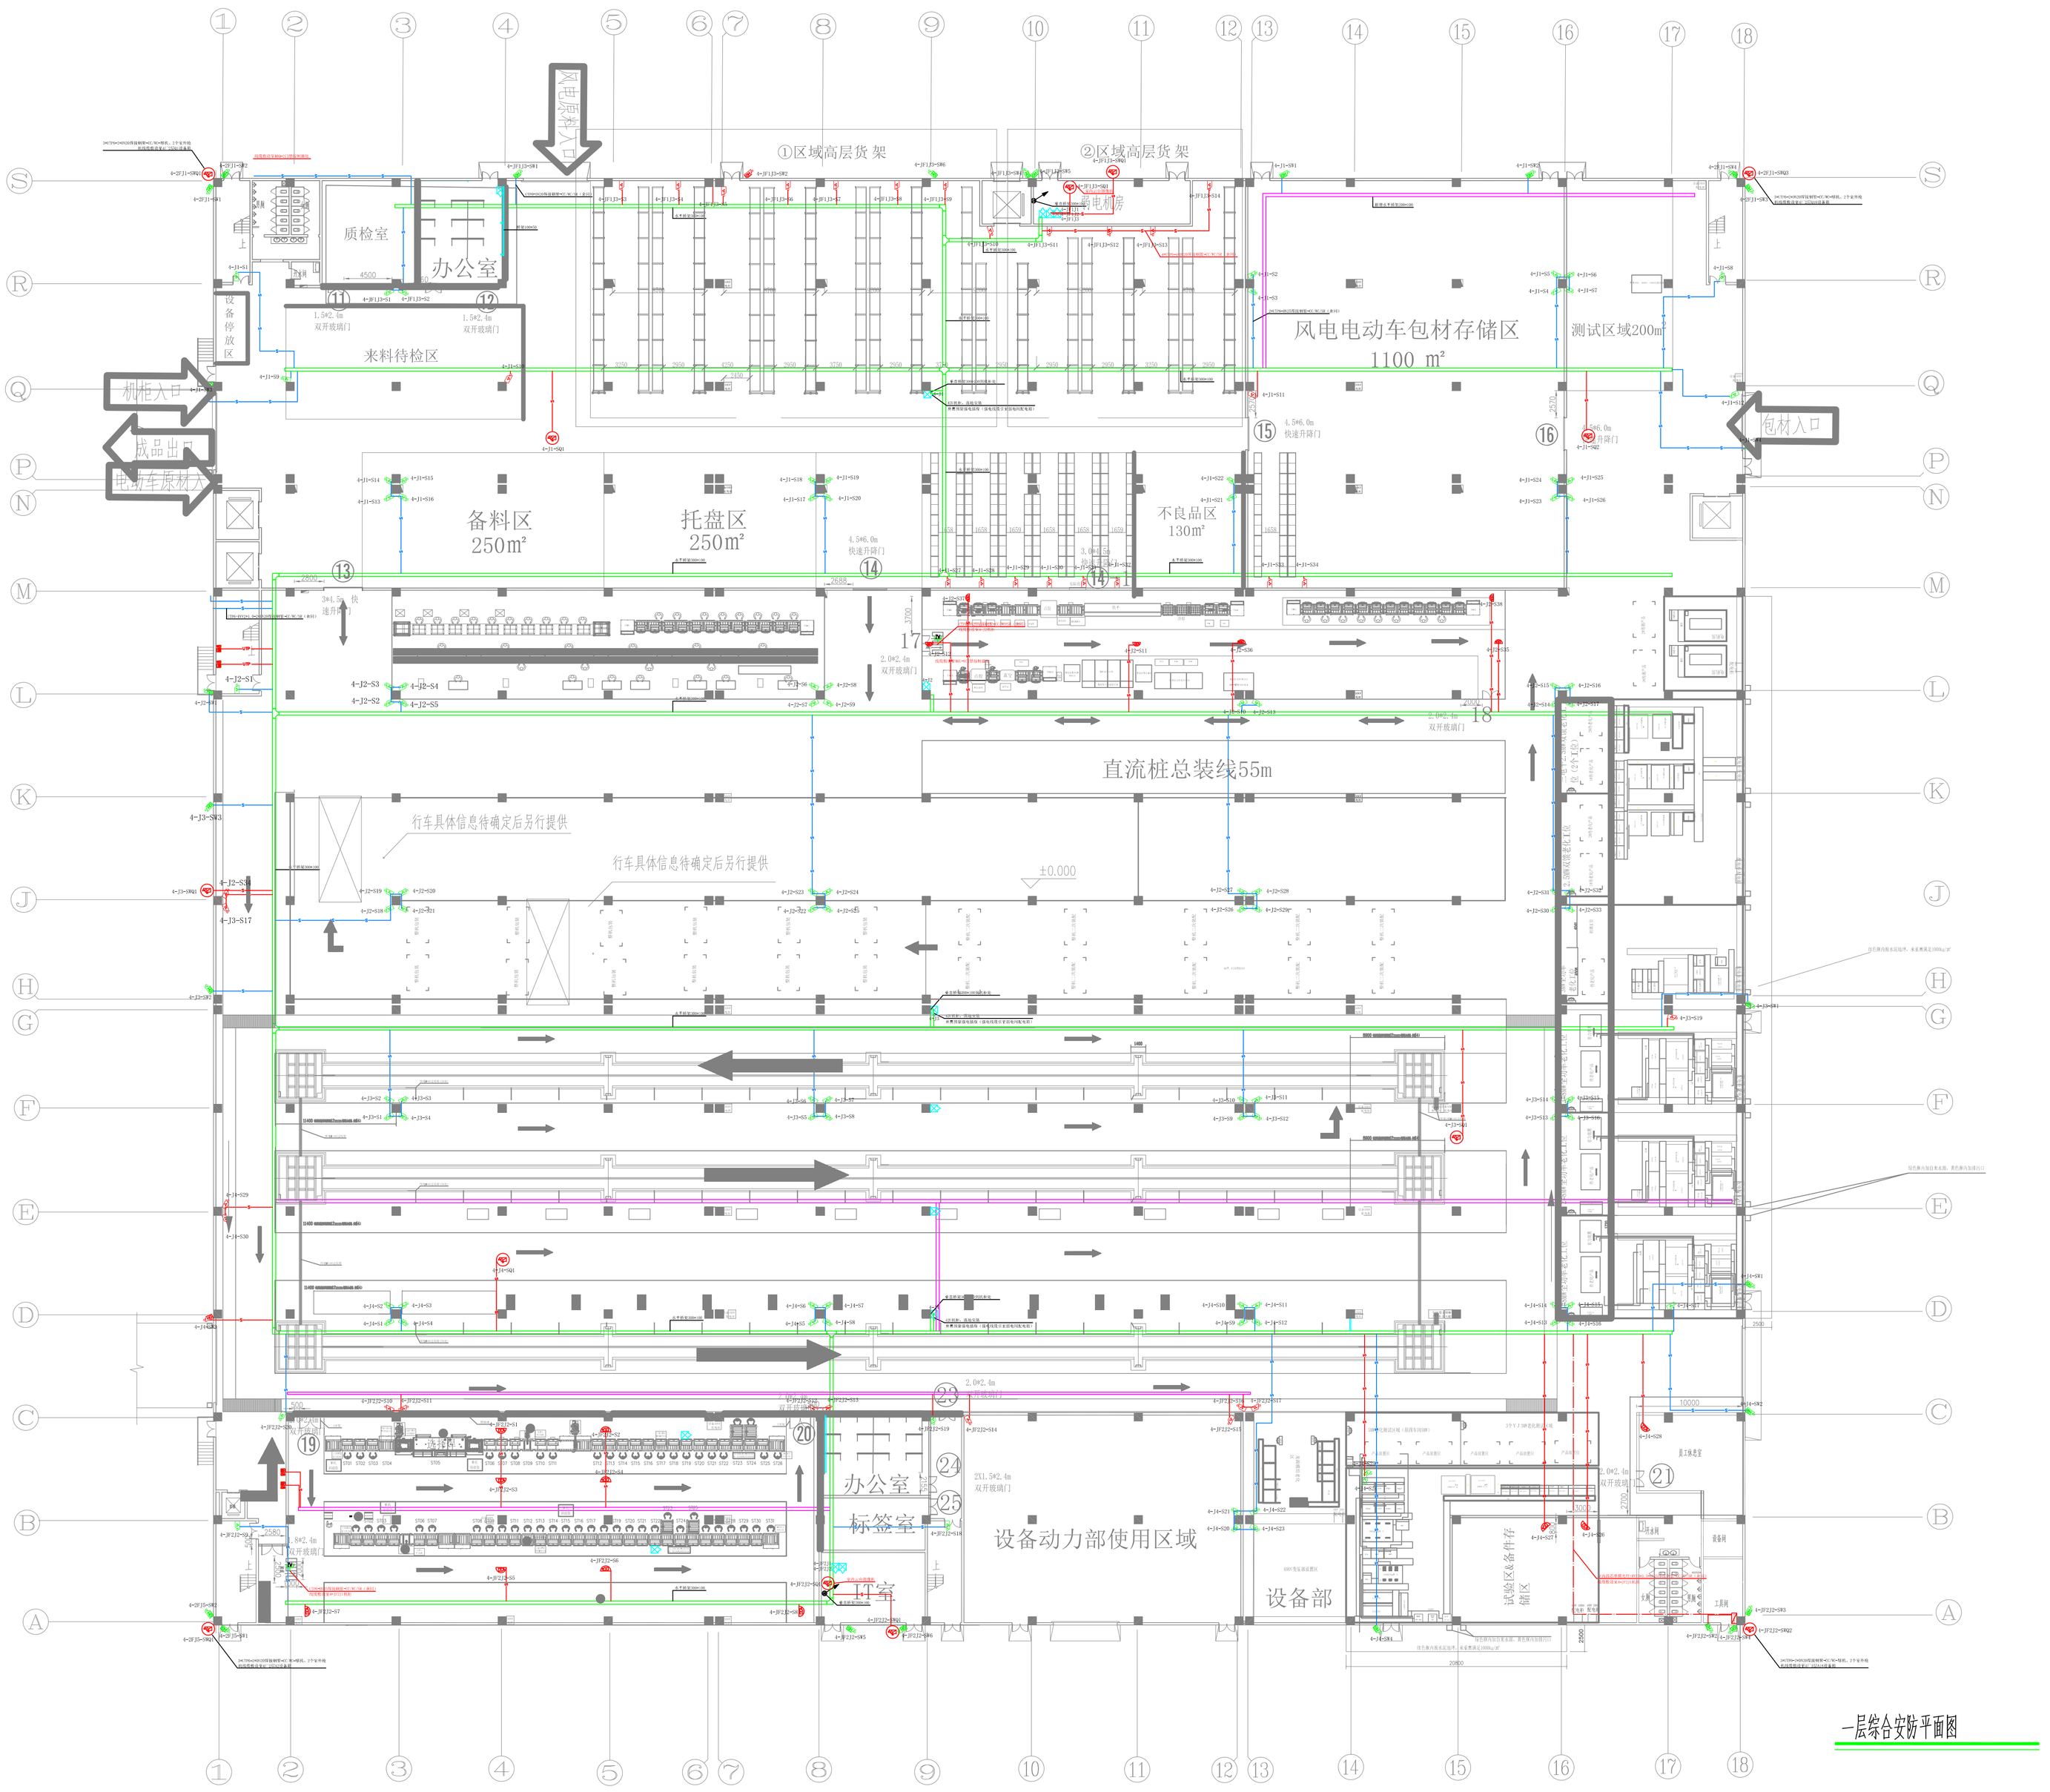

中机第一设计研究院有限公司
First Design and Research Institute MI China Co., Ltd.

工程设计证书
编号：A134004086
工程咨询证书
工咨甲21420070007

附 注
ANNOTATION

出图签章
DRAWING SEAL

执业签章
REGISTERED ENGINEERS' SEAL

本图须加盖本院出图签章、执业签章，否则一律无效
DRAWINGS SHALL BE CONSIDERED NULL AND VOID WITHOUT DRAWING SEAL AND REGISTERED ENGINEERS' SEAL

项目总设计师	张建宝			
项目总设计师 CHIEF DESIGNER	曹磊			
审 定 APPROVED BY	崔青松			
审 核 VERIFIED BY	陶冶			
校 对 CHECKED BY	丁丽			
专业负责人 PROJECT SUPERVISOR	袖宇阳			
设 计 人 DESIGNED BY	白雨冰			
	姓 名 NAME	签 字 SIGNATURE	月	日

建设单位 CLIENT：阳光电源股份有限公司

建设地点 SITE：安徽省 合肥市

工程名称 PROJECT NAME：阳光电源股份有限公司
新能源发电成套装备智造基地二期项目

项目名称 SUB-PROJECT NAME：厂房四

图纸内容 CONTENT OF DRAWINGS：一层综合安防平面图

比例 PROPORTION	1:300	阶段 STAGE	施工图
日期 DATE	2020年12月	版次 EDITION No.	第一版
专业 PROFESSION	电气		

图号 DRAWING No. AH283H11-DC050-103